



सत्यमेव जयते

INDIA NON JUDICIAL Government of Uttar Pradesh



IN-UP29641108063923Y



e-Stamp

Acc Name- No. 10365
226
Sharma


Stamp Vendor

Licence No. 10365

E-Stamping Acc Id-UP14401904

Stamp Vendor Dis. Area

Certificate No. : IN-UP29641108063923Y
Certificate Issued Date : 13-Aug-2026 03:07 PM
Account Reference : NEWIMPACC (SV)/ up14401904/ FATEHABAD/ UP-AGR
Unique Doc. Reference : SUBIN-UPUP1440190451939133833459Y
Purchased by : DHARMENDRA SO DAUDAYAL
Description of Document : Article 33 Gift - Registerable
Property Description : A PLOT MOHALLA TOLA PART OF GATA NO 219 KASWA SHAMSHABAD TEHSIL FATEHABAD DIST AGRA
Consideration Price (Rs.) :
First Party : DHARMENDRA SO DAUDAYAL
Second Party : LAKSHMI WO DHARMENDRA
Stamp Duty Paid By : DHARMENDRA SO DAUDAYAL
Stamp Duty Amount(Rs.) : 5,000
(Five Thousand only)

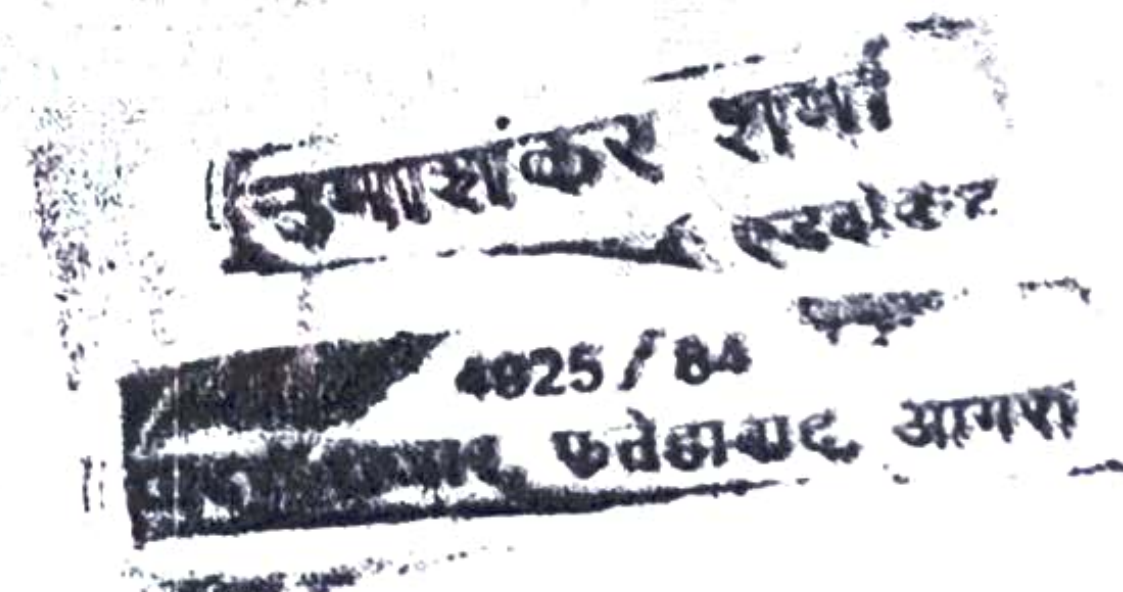

Signature/Text type below this line

धर्मेश्वर

मि. लक्ष्मी

0028825951

Statutory Alert:

(1) The amount of stamp duty value entered on the e-Stamp is payable in any form for the purchase of e-Stamp. (2) If the above information/declaration is found to be false or incorrect, it shall be punishable under the provisions of the law. (3) The authority before whom the document is presented shall ensure that the e-Stamp is being used for the purpose and in the name for which it was purchased. (4) The authenticity of this Stamp certificate should be verified at www.shoilestamp.com or using the official mobile app of Shoile Stamp. Any discrepancy in the details on this Certificate and as available on the website/Mobile App renders it invalid.

10365/2026



नि. लक्ष्मी

लेखपत्र का संक्षिप्त विवरण

1- भूमि का प्रकार	एक किता भूखण्ड मय कमरा
2- वार्ड / परगना	फतेहाबाद जिला आगरा
3- मौहल्ला / ग्राम	मौहल्ला टोला कस्बा शमसाबाद
4- सम्पत्ति का विवरण	गाटा संख्या 219 का जुज भाग
5- मापन की इकाई	वर्ग मीटर
6- सम्पत्ति का क्षेत्रफल	186.04 वर्ग मीटर
7- सड़क की स्थिति	9 मीटर से कम चौड़े मार्ग पर स्थित
8- अन्य विवरण	नहीं
9- सम्पत्ति का प्रकार	आवासीय भूखण्ड
10- सम्पत्ति का कुल क्षेत्रफल	नहीं
11- कुल आच्छादित क्षेत्रफल	18.60 वर्गमीटर गाटर पटिया से निर्मित
12- स्थिति फिनिश आदि	नहीं
13- पेड़ों का मूल्यांकन	नहीं
14- बोरिंग / कुआ / अन्य	नहीं
15- निर्मित क्षेत्रफल	18.60 वर्गमीटर गाटर पटिया से निर्मित
16- निर्माण का वर्ष	2020
17- सह0 आ0 स0 के सदस्य	नहीं
18. प्रतिफल की धनराशि	0/-रु0

व. भू. वि.

नि. लक्ष्मी

चौहददी

पूरव- रास्ता 12 फीट चौड़ा
पश्चिम- मकान रमेशचन्द्र
उत्तर- खाली प्लाट संजू
दक्षिण- प्लाट खाली रविन्द्र

प्रथमपक्ष/हिबैकर्ता की संख्या-1

धर्मेन्द्र पुत्रश्री दाऊदयाल निवासी मौहल्ला टोला कस्बा शमसाबाद तहसील फतेहाबाद
जिला आगरा। मो0- 9761122053

आधार कार्ड नं0- XXXX XXXX 4489 पैन नं0- FPUPD2836H

द्वितीयपक्ष/हिबैगृहीता की संख्या-1

लक्ष्मी पत्नीश्री धर्मेन्द्र निवासी मौहल्ला टोला कस्बा शमसाबाद तहसील
फतेहाबाद जिला आगरा। मो0- 9761122053

आधार कार्ड नं0- XXXX XXXX 2680 पैन नं0- CEIPL7871N

हिबैनामा- 0/-

सरकारी मालियत- 16,66,000/-रु0

सर्किल रेट- 7,500/-रु0 प्रति वर्ग मीटर खाली भूखण्ड की दर

14,000/-रु0 प्रति वर्ग मीटर गाटर पटिया से निर्माण दर

स्टाम्प- 5,000/-रु0 पति-पत्नी

ई-स्टाम्प नं0- IN-UP29641108063923Y

विक्रय सम्पत्ति- एक किता भूखण्ड मय कमरा क्षेत्रफल 186.04 वर्ग मीटर
{ रेटलिस्ट के पृष्ठ संख्या 12 कोड 1 के अनुसार 9 मीटर कम चौड़े मार्ग
के सहारे स्थित }

द्वितीयपक्ष



प्रथमपक्ष



विदित हो कि प्रथमपक्ष/दानदाता एक किता आवासीय खाली भूखण्ड बाकै मौहल्ला टोला कस्बा शमसाबाद तहसील फतेहाबाद जिला आगरा, जो कि गाटा संख्या 219 का जुज भाग है, जिसकी पैमाइश पूरब से पश्चिम 100 फीट व उत्तर से दक्षिण 20 फीट क्षेत्रफल 2000 वर्गफीट यानी 186.04 वर्गमीटर है, जिसकी चौहद्दी पृष्ठ संख्या 3 पर अंकित है का मालिक काविज व दखील है। जिसमें 20×10 फीट यानी 200 वर्गफीट अर्थात् 18.60 वर्गमीटर में एक कमरा गाटर पटिया से निर्मित है तथा शेष भूखण्ड खुला व खाली है जिसकी करीबन 1,500 ईंटों से 5 फीट ऊँची बाण्डड़ी हो रही है। उक्त भूखण्ड प्रथमपक्ष की माँ माया देवी पत्नी दाउदयाल ने श्रीमती मनोरमा देवी पत्नी शान्ती स्वरूप से बजरिए बैनामा दिनांक 28.06.2013 द्वारा क्रय किये गये भूखण्ड का जुज भाग है। जिसकी रजिस्ट्री बही संख्या 1 जिल्द संख्या 2497 के पृष्ठ 293/372 में नम्बर 4715 दिनांक 29.06.2013 को हुई है। प्रथमपक्ष की माँ माया देवी पत्नी दाउदयाल की मृत्यु के बाद उक्त पैमाइशी भूखण्ड मुझ प्रथमपक्ष को बजरिए उत्तराधिकार में प्राप्त हुआ है। इस प्रकार प्रथमपक्ष को उक्त भूखण्ड के सम्बन्ध में पूर्ण अधिकार मालिकाना व हस्तान्तरण आदि प्राप्त है। कोई भागी या अंशी माने इंतकाल के नहीं है। प्रथमपक्ष को अपनी पत्नी द्वितीयपक्ष से काफी प्रेम व स्नेह है तथा वह मेरी सेवा सुश्रुषा करती है तथा मुझे हर प्रकार से आराम दे रही है। अतः मैं प्रथमपक्ष अपने उक्त वर्णित पैमाइशी भूखण्ड को द्वितीयपक्ष को उपहार स्वरूप दान में देना चाहता हूँ ताकि भविष्य में कोई भी शख्स अथवा अन्य व्यक्ति उसके मालिक होने में कोई उजर न कर सके। अतः मैं अपने जीवनकाल में ही उक्त वर्णित भूखण्ड को

दावेद



मि. ल. इ. गे



द्वितीयपक्ष को उपहार स्वरूप दान देना चाहता हूँ जिसके लिए प्रथमपक्ष ने द्वितीयपक्ष से उक्त भूखण्ड को उपहार स्वरूप दान में देने की इच्छा जाहिर की तो उन्होंने उक्त भूखण्ड को दान में लेना स्वीकार कर लिया है अतः मैं प्रथमपक्ष अपनी पूर्ण स्वेच्छापूर्वक व चैतन्यावस्था में न खाये पीये कोई नशीली वस्तु के विला किसी धौंस व दबाब आदि के अपने उपरोक्त वर्णित पैमाइशी भूखण्ड क्षेत्रफल 186.04 वर्गमीटर को द्वितीयपक्ष के हक में उपहार स्वरूप दान में दे दिया व द्वितीयपक्ष/दानग्रहीता ने दान स्वीकार कर लिया है तथा कब्जा व दखल भौतिक रूप से द्वितीयपक्ष को दे दिया है तथा द्वितीयपक्ष उपरोक्त भूखण्ड पर काविज व दखील हो गई है। प्रतिज्ञा यह कि हिबैगृहीता/द्वितीयपक्ष आज से उक्त भूखण्ड की पूर्ण मालिक हुई चाहे जिस प्रकार उपरोक्त भूखण्ड का मालिकाना हक व हस्तान्तरण आदि प्रयोग में लावें। उपरोक्त भूखण्ड मुवैया के दरवाजे, नाली, तोड़े, छज्जे, परनाले, खिड़की इत्यादि रास्ते की तरफ की निकाले जा सकेंगे। प्रथमपक्ष व वारिसान प्रथमपक्ष को उक्त हिबैशुदा भूखण्ड से कोई सम्बन्ध व सरोकार नहीं रहा न भविष्य में रहेगा। वाद रजिस्ट्री हिबैगृहीता इसका नामान्तरण नगर पालिका अभिलेखों में अपने नाम दर्ज कराले। उसमें हिबैकर्ता/प्रथमपक्ष को कोई ऐतराज व उजर नहीं होगा। हिबैशुदा भूखण्ड नजूल, वक्फ, पट्टा, ग्राम समाज व सरकारी आस्थान की सम्पत्ति नहीं है। यदि भविष्य में कोई भी व्यक्ति/परिवारिजन अथवा मेरा कोई पुत्र हिबैशुदा भूखण्ड में अपना हक/दावा करें अथवा द्वितीयपक्ष के मालिक होने में कोई उजर व दावा करें तो उस शख्स का वह उजर व दावा रोबरू अदालत व पंचान के झूठा व अमान्य समझा जावे। अतः प्रथमपक्ष ने अपने जीवन काल

द्वितीयपक्ष



प्रथमपक्ष



में ही द्वितीयपक्ष को उक्त भूखण्ड पर पूर्ण मालिक काविज व दखील कर दिया है तथा हिबैशुदा भूखण्ड में प्राप्त सभी अधिकार जो आज तक प्रथमपक्ष को प्राप्त थे वह सभी अधिकार आज की तारीख से बजानिव द्वितीयपक्ष मुन्तकिल हुए। द्वितीयपक्ष उक्त भूखण्ड को चाहे जिसे चाहे जैसे विक्रय, दान, बन्धक करें अथवा अपनी आवश्यकतानुसार बैंक/वित्तीय संस्था से ऋण आदि प्राप्त करें तथा उसका भुगतान करें उसमें प्रथमपक्ष व वारिसान को कोई उजर न होगा। भूखण्ड मौहूवा नगर पालिका शमसाबाद के अन्तर्गत मौहल्ला टोला में 9 मीटर से कम चौड़े मार्ग के सहारे स्थित है। जिसकी सर्किल रेट नियत रेटलिस्ट के पृष्ठ संख्या 11 क्रमांक 2 के अनुसार निर्धारित दर 7,500/-रुपया प्रति वर्ग मीटर से भूखण्ड की सरकारी मालियत 13,96,000/-रु० व इसमें गाटर पटिया से निर्मित क्षेत्रफल 18.60 वर्गमीटर की निर्माण दर 14,000/-रु० प्रति वर्गमीटर से निर्माण लागत 2,61,000/-रु० व इसमें 1500 ईंटों से हो रही बाउण्ड्री की निर्माण लागत 9,000/-रु० लगाई गई है। इस प्रकार हिबै भूखण्ड मय कमरा की कुल सरकारी मालियत 16,66,000/-रु० होती है। जिस पर पति-पत्नी होने के कारण शासनादेश संख्या 18/2023/995/94-एस०आर०-2-2023- 700(29)/2021 दिनांक 03 अगस्त 2023 के अनुसार 5,000/-रु० का स्टाम्प अदा किया जा रहा है। जिसमें राजस्व का सरासर फायदा है तथा स्टाम्प एक्ट की धारा 27 का अनुपालन किया गया है। हिबैशुदा भूखण्ड पूर्ण रूप से पाक व साफ है तथा उपरोक्त भूखण्ड मुवैया का नक्शा व स्थलफोटो दस्तावेज हाजा के साथ संलग्न है। पक्षगण की सनाख्त/पहिचान गवाही द्वारा की गयी। अतः यह हिबैनामा लिख दिया कि प्रमाण रहे व समय पर काम आवै।

दस्तावेज



निष्कर्ष



हिस्वहिदायत पक्षकारों के निदेशानुसार गवाह लिखे गये हैं तथा गवाहों की शनाख्त के आधार पर पक्षकारों के फोटो प्रमाणित किये गये हैं।

कुरैशी


निलहमी


गवाह-नगीन कुरैशी पुत्र नहीम
कुरैशी निवासी मौहल्ला टोला
कस्बा शमसाबाद तहसील
फतेहाबाद जिला आगरा।

मो0- 8954011414

नगीन कुरैशी



गवाह- संजू पुत्रश्री दाउदयाल
निवासी ग्राम मल्हैला तहसील
फतेहाबाद जिला आगरा।

मो0- 7668457639

सिद्धे पा



नगीन कुरैशी



सिद्धे पा



तहरीर तारीख 13.08.2026ई0 व हिदायत पक्षकारान के व मसौदा उमाशंकर शर्मा एडवोकेट व टाईप द्वारा हिमांशु गुप्ता तहसील फतेहाबाद जिला आगरा।

वकील




निलहमी




उमाशंकर शर्मा
एडवोकेट
4025/84
महेश बाजार, फतेहाबाद, आगरा

SITE PLAN OF A PLOT SITUATED AT
MAUHALLA TOLA KASBA SHAMSABAD
TEHSIL FATEHABAD DISTRICT AGRA
PART OF GATA NO.- 219
AREA IN GIFT- 2000SQ. FTS. (186.04SQ.MTRS)

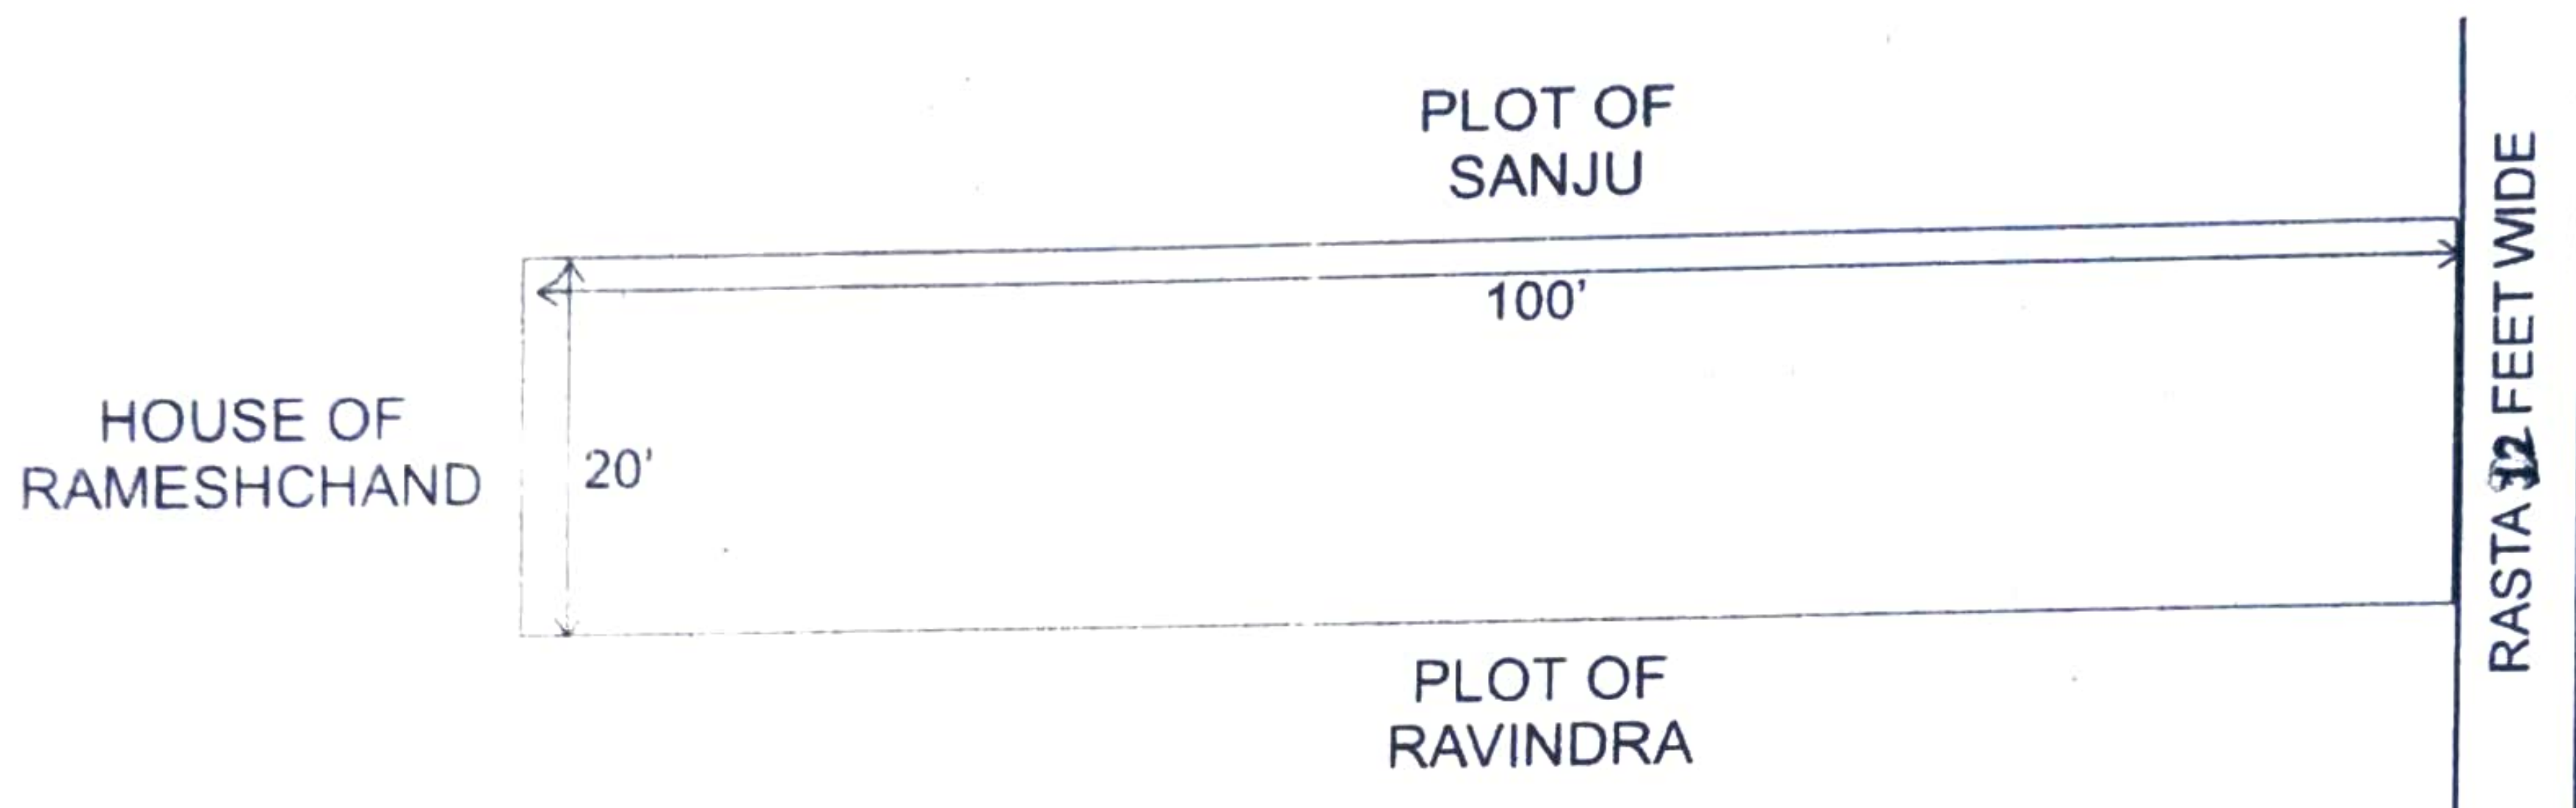


SCALE 1 Inch=20 feet

1ST PARTY- DHARMENDRA

2ND PARTY- LAKSHMI



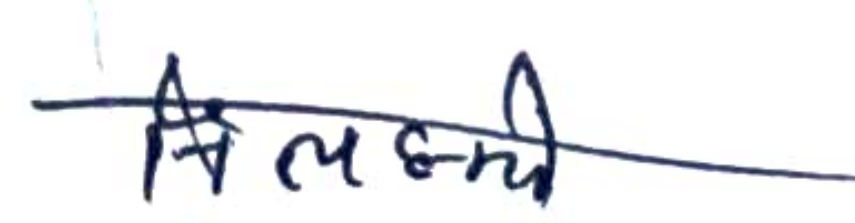


आवेदन सं०: 202600769011719

बही संख्या 1 जिल्द संख्या 7376 के पृष्ठ 19 से 36 तक क्रमांक 10365 पर दिनांक
13/08/2026 को रजिस्ट्रीकृत किया गया।

रजिस्ट्रीकरण अधिकारी के हस्ताक्षर

आशीष कुमार सबसैना प्रभारी
उप निबंधक : फतेहाबाद
आगरा
13/08/2026



::प्रमाणक::

हम प्रमाणित करते हैं कि -:

- i. दानकर्ता के पास भूमि की प्राप्ति का स्रोत:- विरासत में
- ii. दान ग्रहिता से उसका सम्बंध:- पति - पत्नी
- iii. सम्बन्ध का साक्ष्य:- आधारकार्ड
- iv. मृतक भाई की पत्नी का दान ग्रहिता होने के प्रकरण में भाई का मृत्यु प्रमाण पत्र है या नहीं नहीं
- v. सम्बन्धित सम्पत्ति का geotag फोटोग्राफ सलगन है
- vi. "कि इस दान विलेख में हस्तान्तरित की जा रही सम्पत्ति शासनादेश संख्या-18/2023/995/94 एस0आर0-2-2023-700(29)/2021 दिनांक 3 अगस्त 2023 यथा संशोधित के अनुसरण में किया जा रहा है, इस सम्पत्ति को दानदाता द्वारा दानग्रहिता के रूप में शासनादेश में उल्लिखित अवधि के अन्तर्गत प्राप्त नहीं किया गया है, यदि विपरीत तथ्य ज्ञात होते हैं तो जो भी विधिक कार्यवाही होगी वह मुझे मान्य होगी।

दिनांक 13/08/26

स्थान जयपुर

हस्ताक्षर दानदाता

अर्पित



हस्ताक्षर दानग्रहिता

निलक्ष्मी



202600789011719

आवेदन दिनांक

13-08-2026

बही संख्या

लेख पत्र का प्रकार

दान पत्र (परिवार के पक्ष में)

प्रस्तुतकर्ता का विवरण

धर्म

नाम (अंग्रेजी में)

DHARMENDRA

गोबाहुल

8534013566

संपत्ति की सं०

सम्पत्ति की स्थिति का विवरण

जनपद	आगरा	तहसील	फरौहाबाद
ब्लॉक/परगना	नगर पालिका परिषद शमशाबाद	मोहल्ला/गाँव	टोला शमशाबाद
सम्पत्ति का विवरण	गाटा संख्या 219 का जुज भाग		
सम्पत्ति का प्रकार			
सम्पत्ति का प्रकार	आवासीय (अकृषक)		
क्षेत्रफल	186.04	भूमि की इकाई	वर्ग मीटर
उपयोग		सेगमेंट प्रकार	3 से अधिक 9 मी तक चौड़े मार्ग पर निर्धारित दर
सम्पत्ति की स्थिति	निर्मित		

विद्यमान संयोजन संख्या

संपत्ति का डिपॉजिट संख्या

अन्य संसाधन संख्या

राजस्व खाती में भूमि की पुनिक आई टी संख्या

सम्पत्ति मूल्यांकन विवरण

बाजारी मूल्य	242000/-	वास्तविक बाजारी मूल्य	1666000.00/-
कुल देय स्टाम्प शुल्क	16940/-	वास्तविक स्टाम्प शुल्क	5000/-
कुल देय निबंधन शुल्क	16660/-		

निर्माण सूचना

आवासीय विवरण

तला की संख्या	तला का प्रकार	आच्छादित क्षेत्रफल	निर्माण वर्ष	निर्माण की श्रेणी
311 संख्या	भूतल	18.6 वर्ग मीटर	2020	कड़ी, गार्डर, पटिया, डाट प्रथम श्रेणी
3	प्रथम तल	0 वर्ग मीटर		आर०सी०सी० प्रथम श्रेणी

सम्पत्ति की चौहद्दी

पूर्व	पश्चिम	उत्तर	दक्षिण	खसरा संख्या	प्लॉट संख्या / भवन संख्या / दुकान संख्या	संततल नक्शा
रास्ता 12 फीट चौड़ा	प्रकाश रमेशचन्द्र	खाली प्लाट संजु	प्लाट खाली रविन्द्र	219 का जुज भाग		

समस्त संपत्तियों से प्राप्त शुल्क का विवरण

बाजारी मूल्य	242000/-	वास्तविक बाजारी मूल्य	1666000.00/-
कुल देय स्टाम्प शुल्क	16940/-	वास्तविक स्टाम्प शुल्क	5000/-
कुल देय निबंधन शुल्क	16660/-		

ई-स्टाम्प द्वारा अदा किया गया स्टाम्प शुल्क विवरण

प्रमाणपत्र संख्या	जारी करने का दिनांक	ई-स्टाम्प मूल्य
IN-UP29641108063923Y	13/08/2026	5000

अन्य विवरण

18

प्रतिलिपिकरण शुल्क-रु०

60

उपरोक्त में कुल पृष्ठों का संख्या (दोनों तरफ)

आवेदन संख्या	202600769011719	आवेदन दिनांक	13-08-2026
संव्यवहार की प्रकृति	बही संख्या -(1)	लेखपत्र का प्रकार	दान पत्र

पक्षकार का विवरण								
क्रम सं	पक्षकार प्रकार	नाम	पिता / माता /पति / अन्य का नाम	स्थायी पता	व्यवसाय	प्रस्तुतकर्ता	आधार संख्या/पैन संख्या/मोबाइल न०	संलग्न
1	दान दाता	श्री धर्मेन्द्र	पुत्र श्री दाऊदयाल	मौहल्ला टोला कस्बा शमसाबाद तहसील फतेहाबाद जिला आगरा	कृषि	स्वयं	N/A FPUPD2836H 8534013566	
2	दान गृहीता	श्रीमती लक्ष्मी	पत्नी श्री धर्मेन्द्र	मौहल्ला टोला कस्बा शमसाबाद तहसील फतेहाबाद जिला आगरा	कृषि	स्वयं	N/A CEIPL7871N 9528024346	
3	गवाह-प्रथम	श्री नगीन कुरैशी	पुत्र श्री नहीन कुरैशी	मौहल्ला टोला कस्बा शमसाबाद तहसील फतेहाबाद जिला आगरा	कृषि		N/A 8954011414	
4	गवाह-द्वितीय	श्री संजू	पुत्र श्री दाऊदयाल	ग्राम मल्हैला तहसील फतेहाबाद जिला आगरा	कृषि		N/A 7668457639	

नोट*:- उप निबंधक कार्यालय :- फतेहाबाद में आवेदक द्वारा दिनांक 13-08-2026 को "लेखपत्र पंजीकरण हेतु अपॉइंटमेंट" दिनांक:- 13-08-2026, Counter 1, समय :- 03.20 PM - 03.25 PM का चयन सफलतापूर्वक संपन्न हुआ। कृपया दिनांक 13-08-2026, Counter 1, समय :- 03.20 PM - 03.25 PM पर फतेहाबाद उप निबंधक कार्यालय में उपस्थित होकर रजिस्ट्री का कार्य पूर्ण कराने का कष्ट करें।